
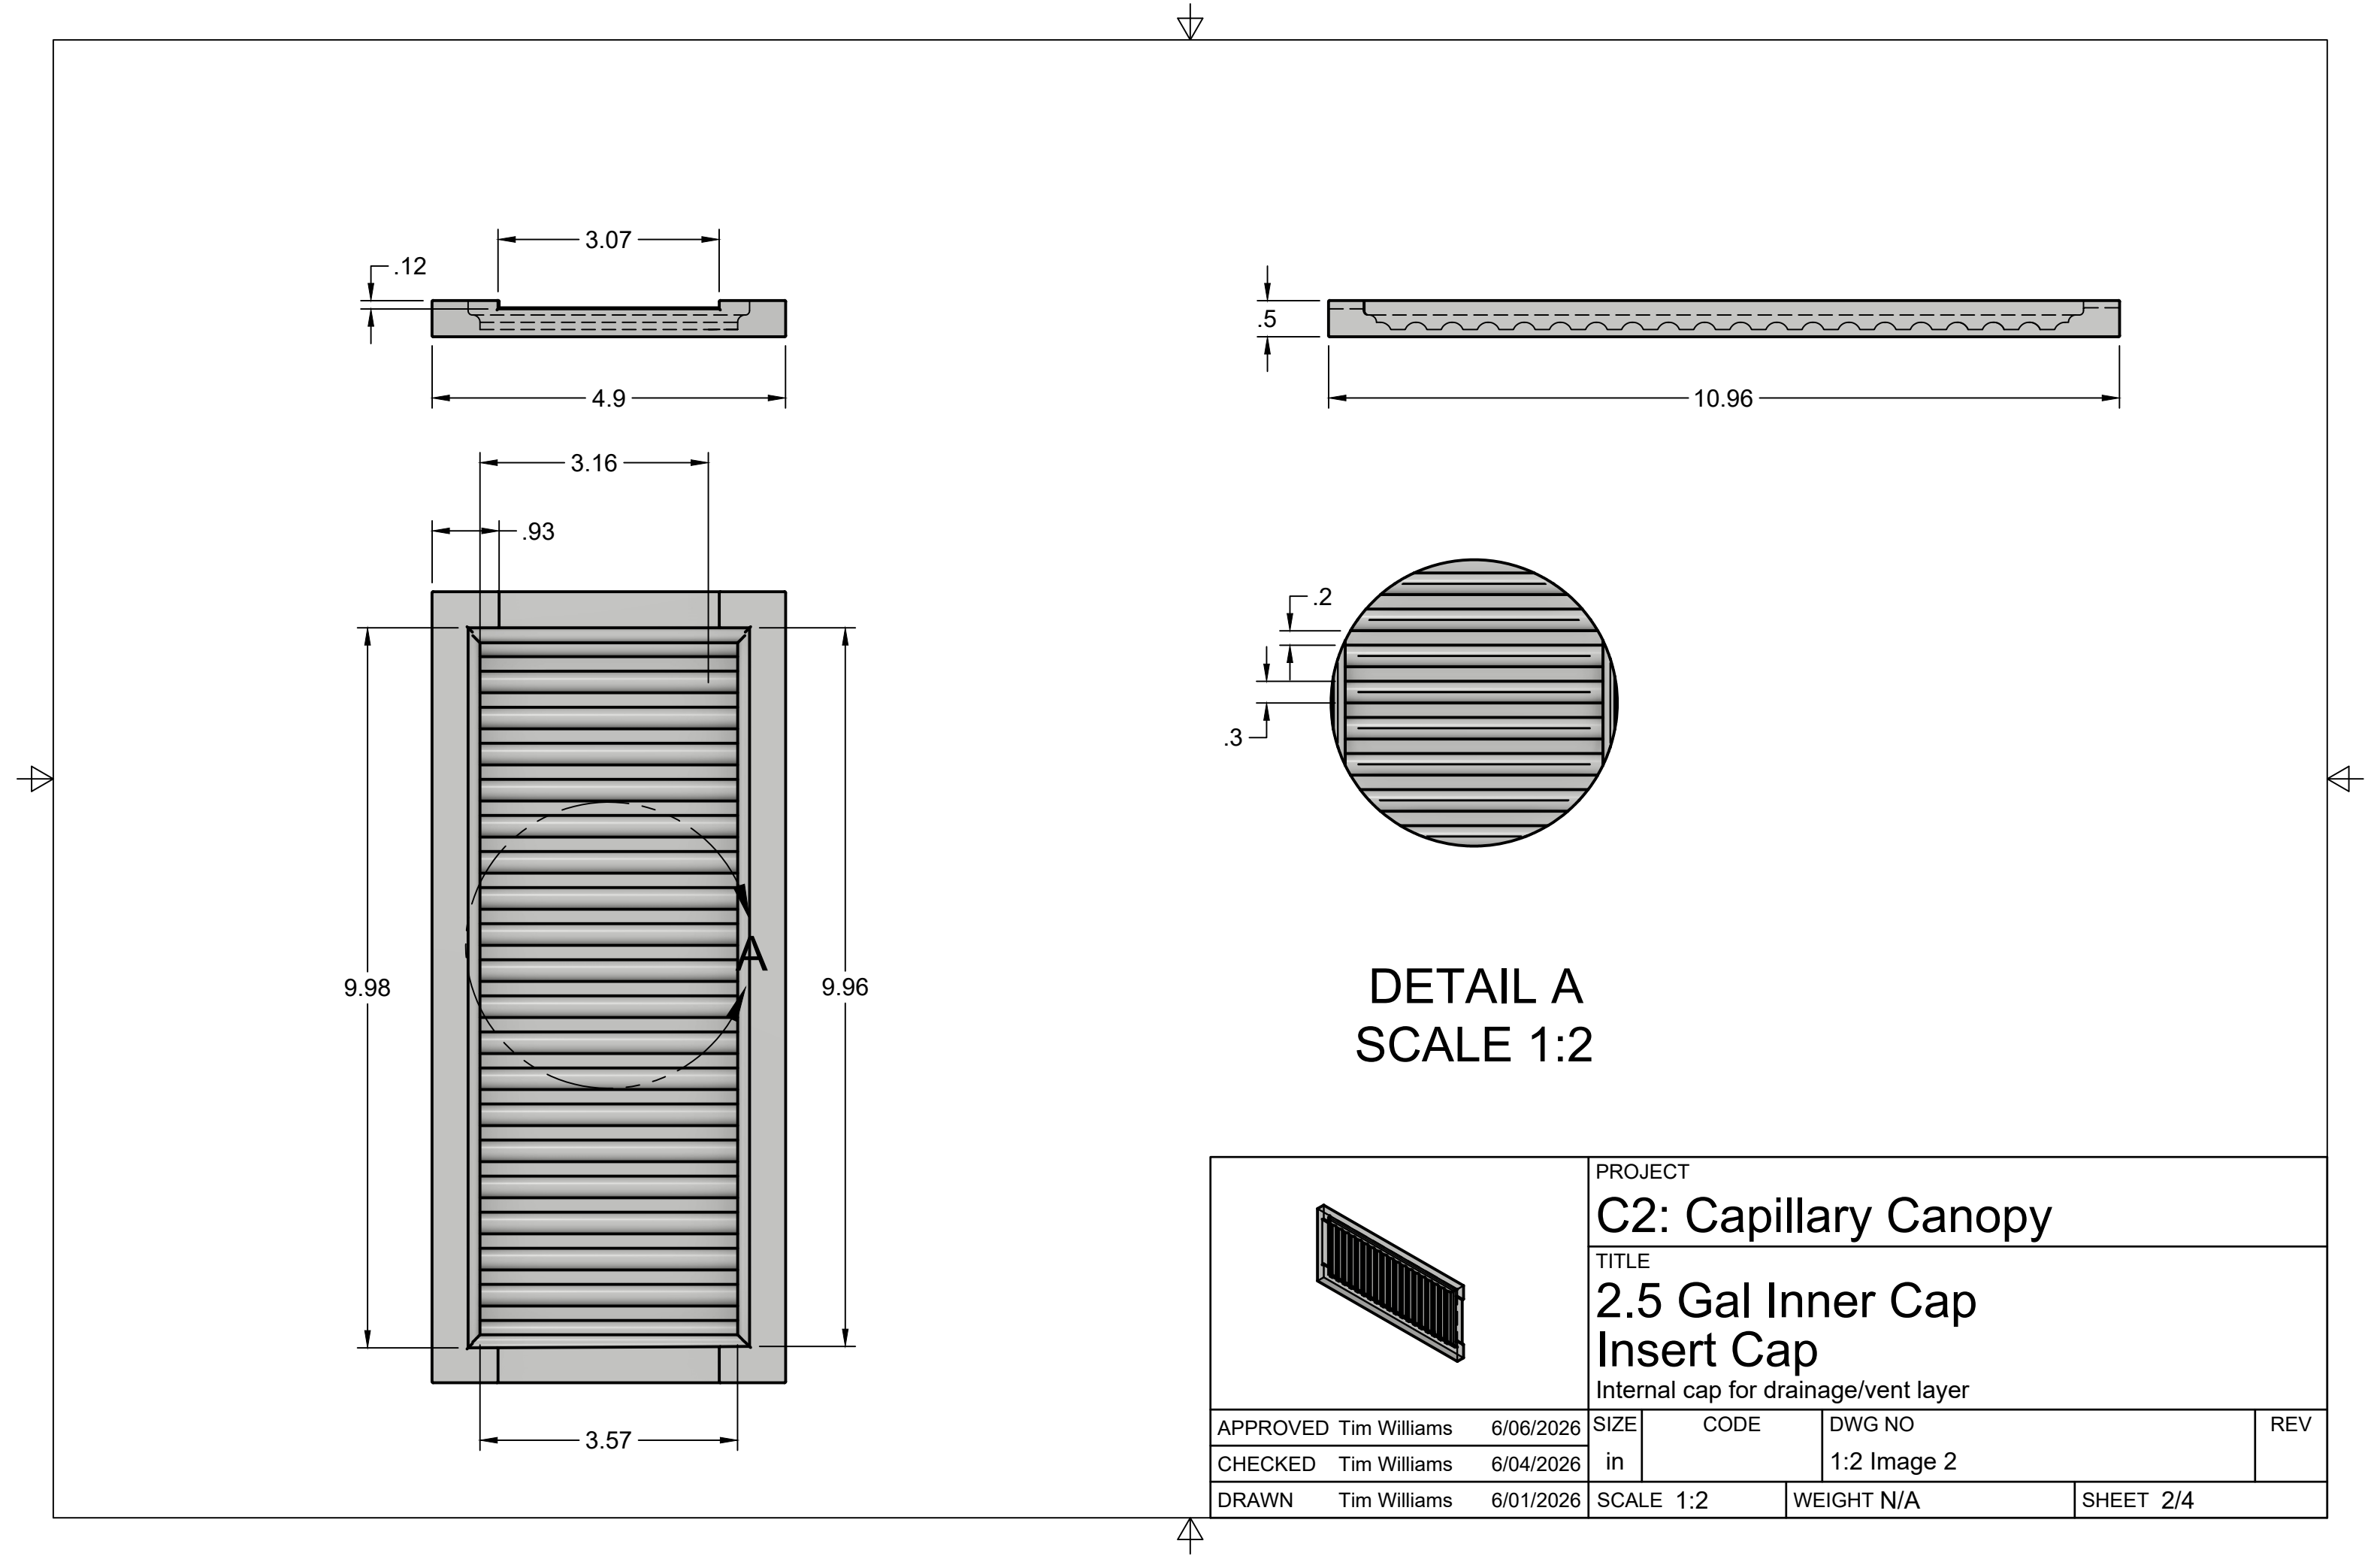


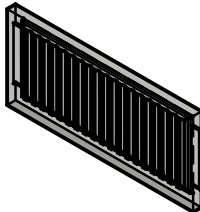

	PROJECT					
	C2: Capillary Canopy					
	TITLE					
2.5 Gal Inner Cap						
Insert Cap						
Internal cap for drainage/vent layer						
APPROVED	Tim Williams	6/06/2026	SIZE	CODE	DWG NO	REV
CHECKED	Tim Williams	6/04/2026	in		1:2 Image 2	
DRAWN	Tim Williams	6/01/2026	SCALE	1:2	WEIGHT N/A	SHEET 2/4